



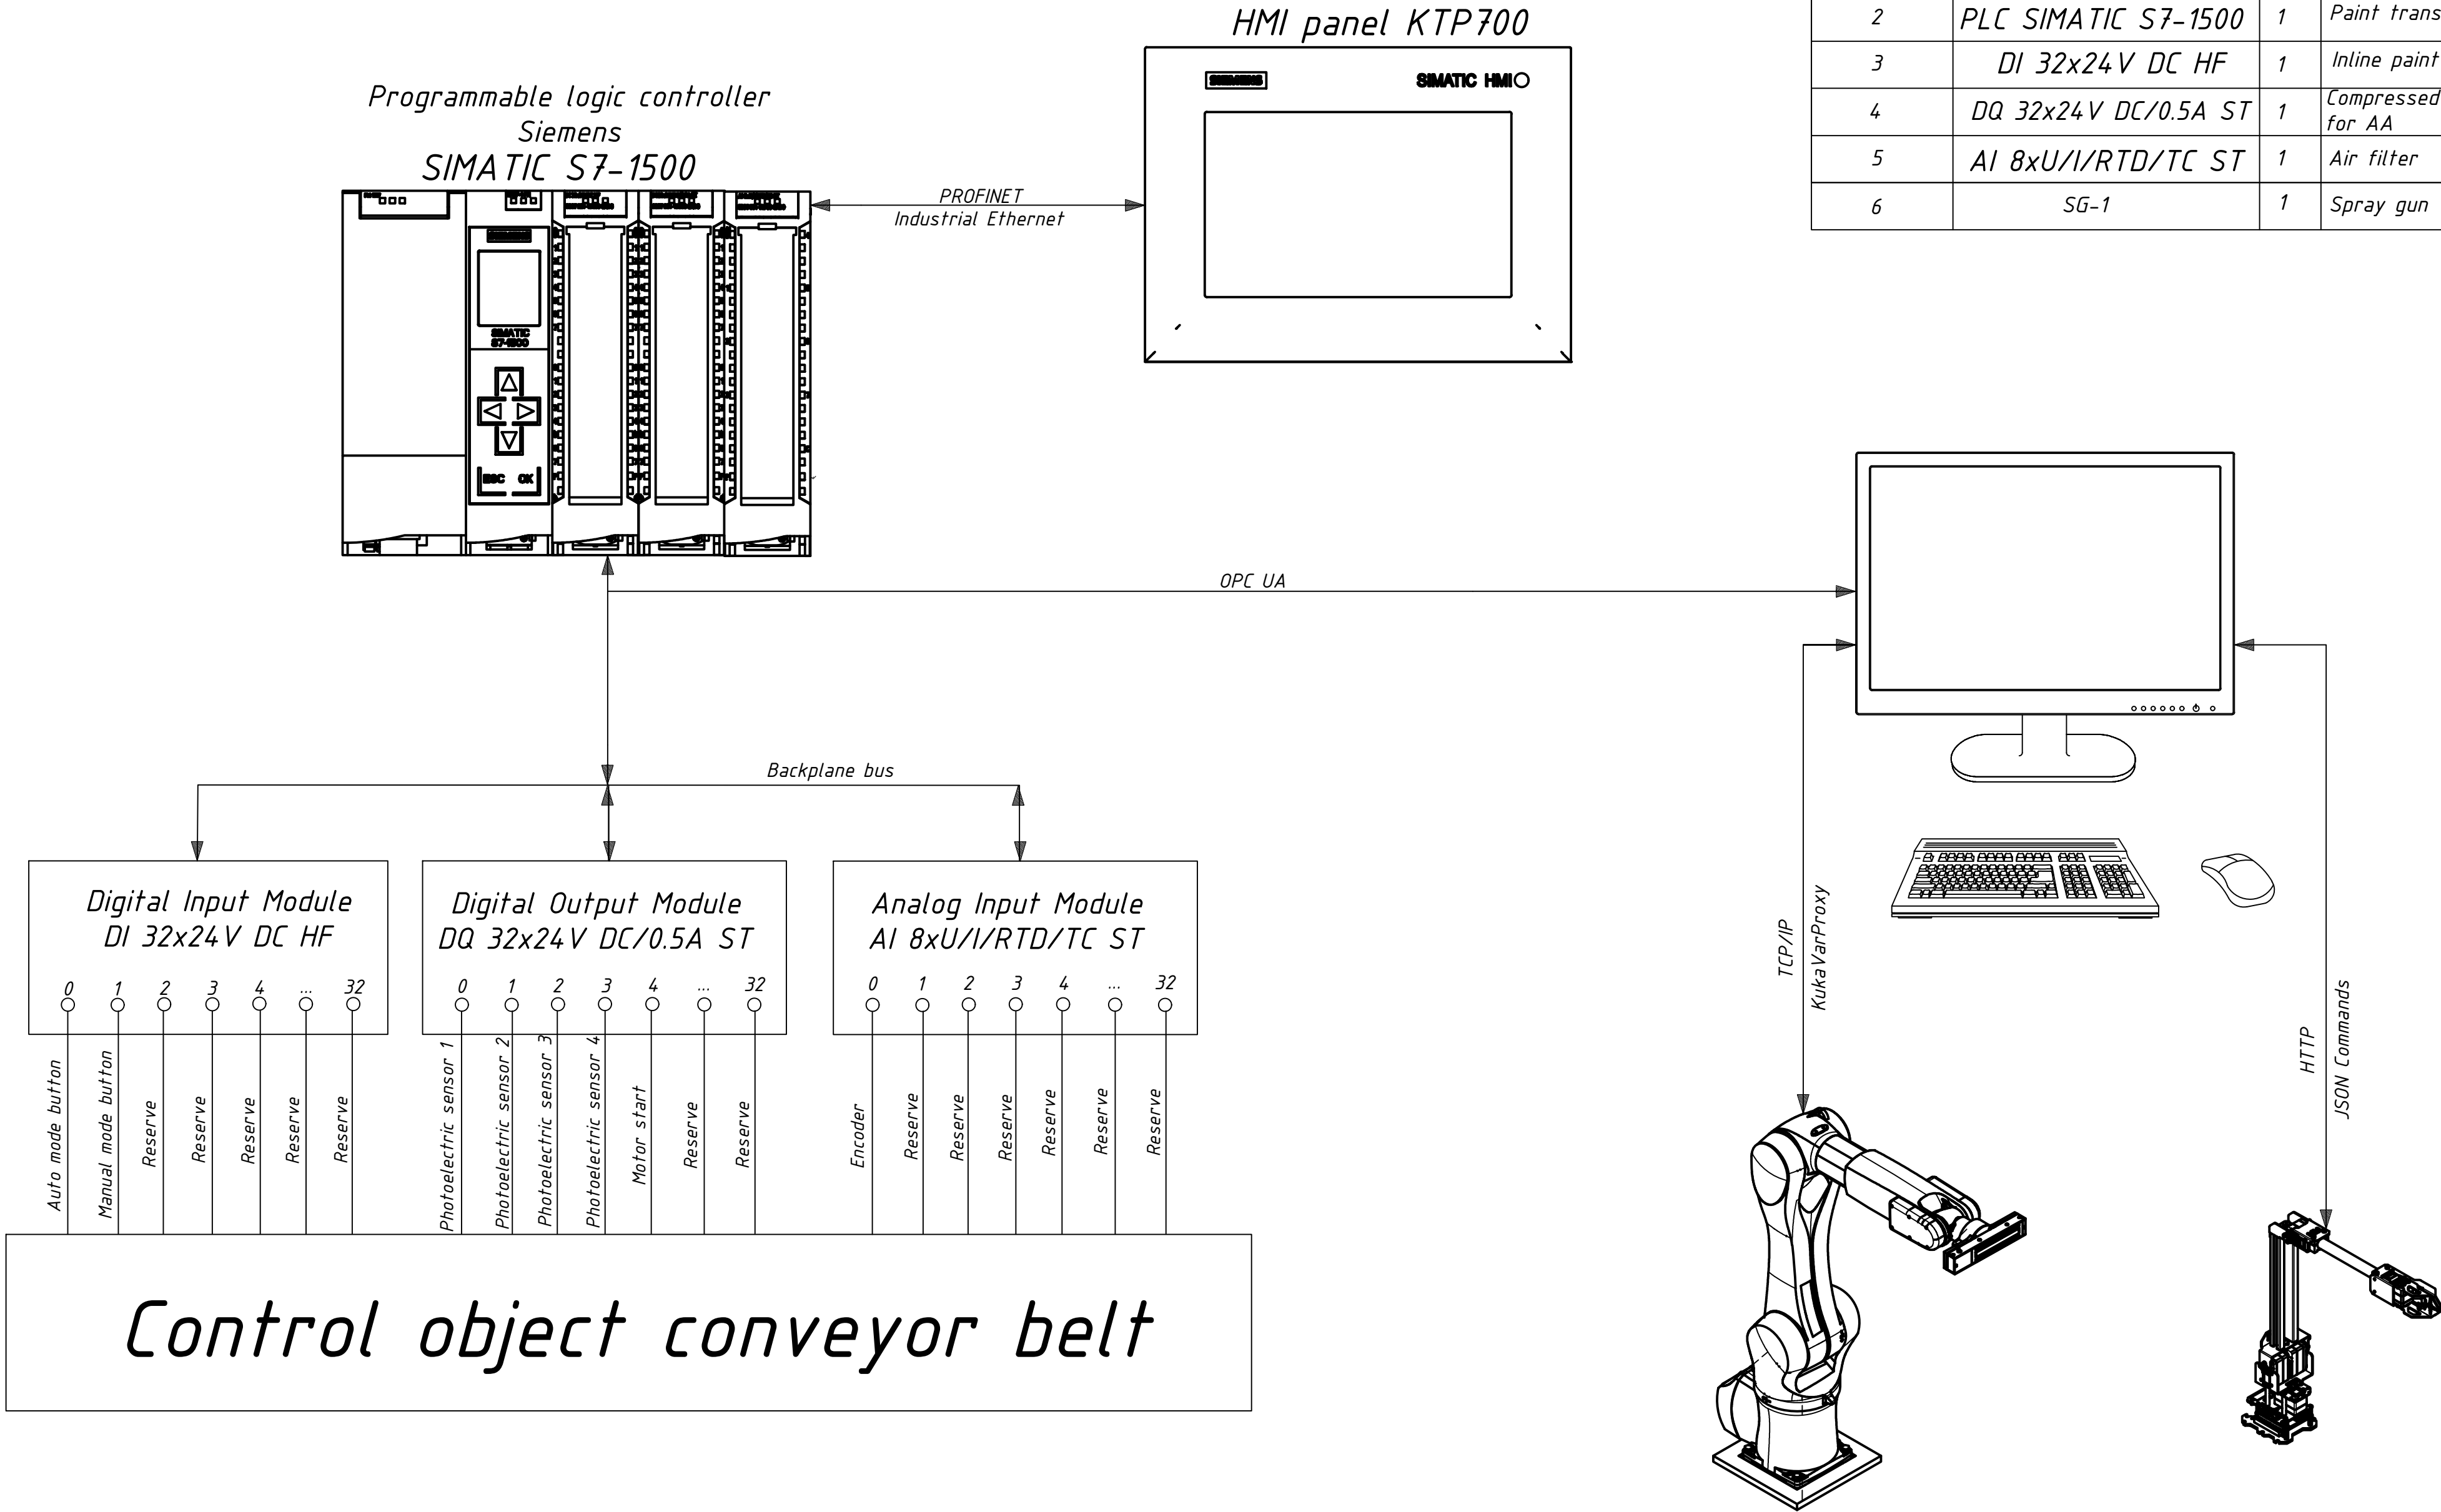

Number	Name	Qty	Notes
1	HMI panel KTP700	1	Paint feed/storage tank
2	PLC SIMATIC S7-1500	1	Paint transfer pump
3	DI 32x24V DC HF	1	Inline paint filter
4	DQ 32x24V DC/0.5A ST	1	Compressed air source for AA
5	AI 8xU/I/RTD/TC ST	1	Air filter
6	SG-1	1	Spray gun

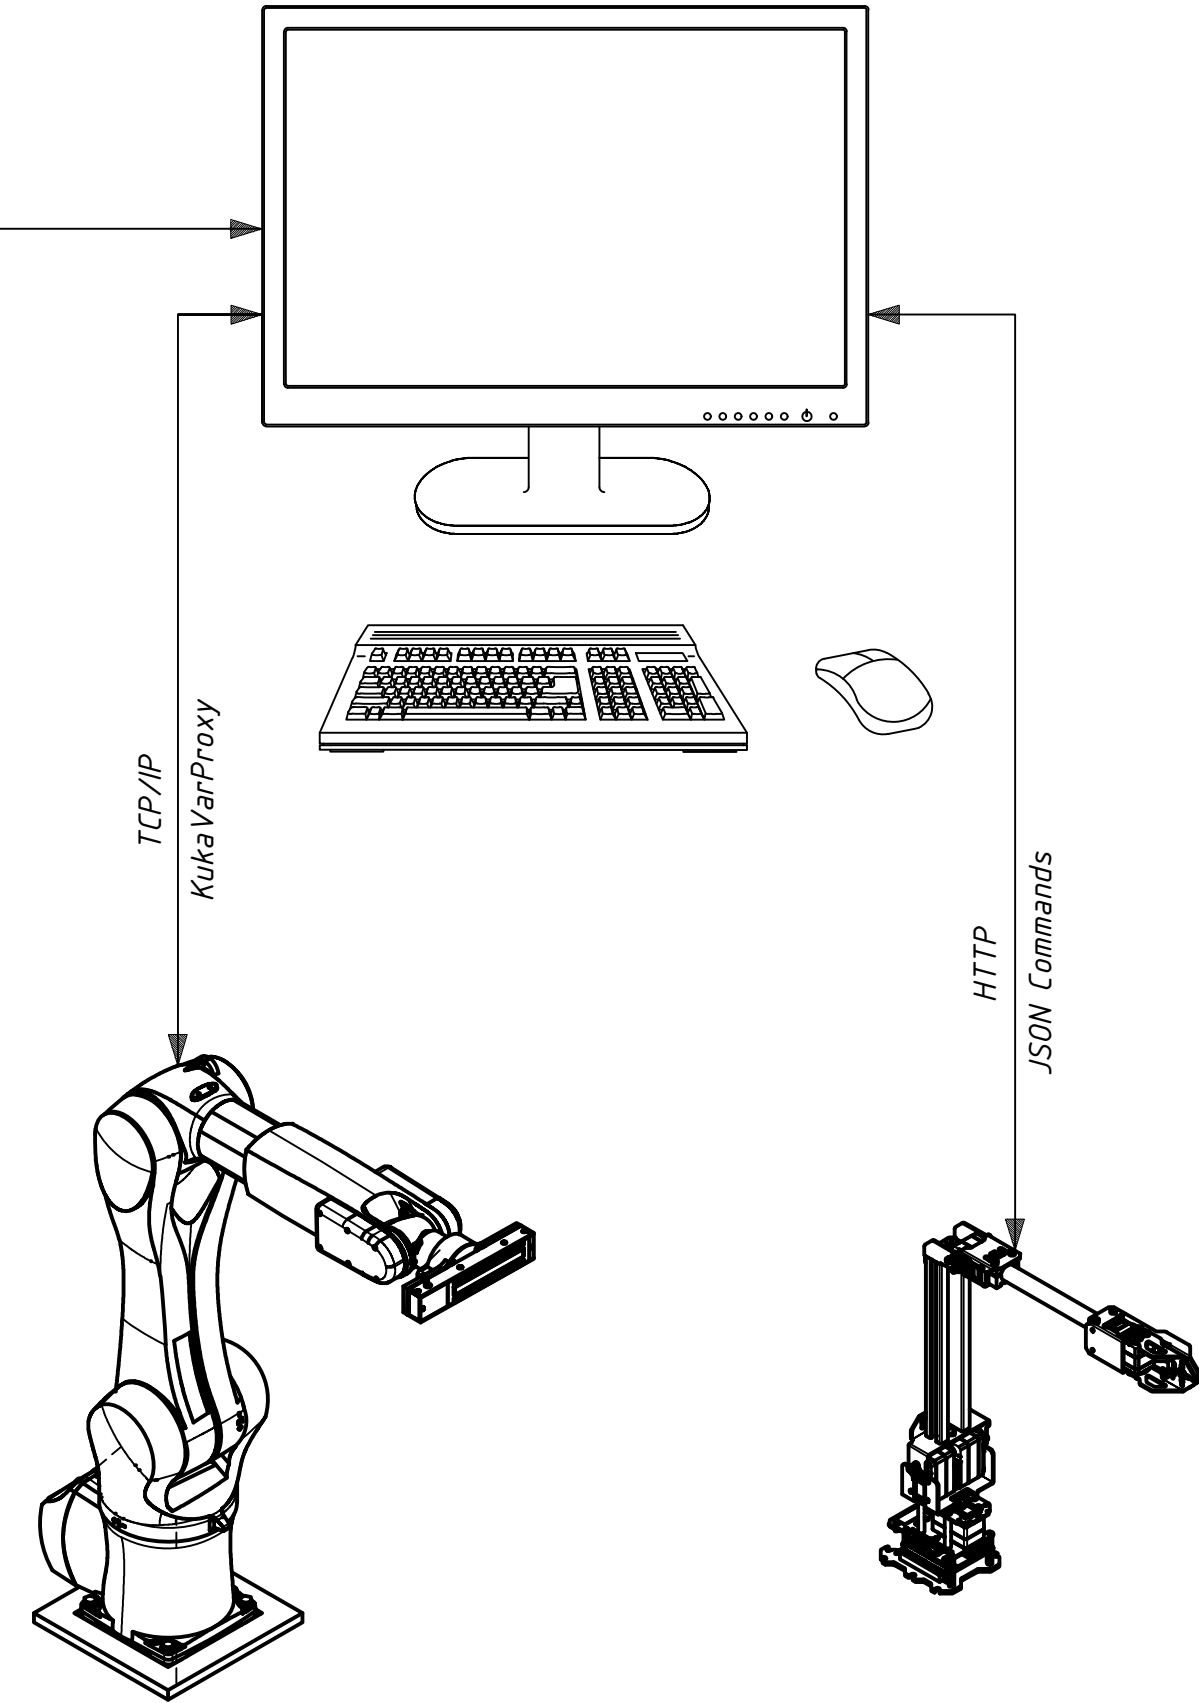

--	--	